

PORTFOLIO

ARCHITECTURE&INTERIOR DESIGN

LINKS

Linkedin - www.linkedin.com/in/malavika-nair-b4a286235

REFERENCES

Available upon request



MALAVIKA NAIR
ARCHITECT | CA/2024/175001

PERSONAL

Name	Malavika Nair
DOB	26th October 1997
Nationality	Indian
Languages	English, Malayalam, Hindi, Tamil

CONTACT

Mobile	+91 7676878778
Home	+91 9986928269
G-mail	malavika.arch@gmail.com
Address	House no 34, Nikunj, 1st Cross, Sector A, Ramaiah Reddy Colony, Basavanagar, Bengaluru, Karnataka, 560037.

ABOUT ME

Architect with 4.5+ years of experience in architectural and interior fit-out projects across GCC and India. Experienced in construction documentation, IFC drawing packages, consultant coordination, and on-site execution. Strong technical background in delivering commercial, corporate, residential, and hospitality projects from concept through handover.

EXPERIENCE

Nov 2016	Hosted KOCHI MUZIRIS BIENNALE 2016.
Jan 2017	Hosted 72 Hours National Symposium, Kaam 1.0 (NASA workshop series), Published 'Synagogues Of Kerala'. (Documentation), - DC school of Architecture & Design).
Feb 2018	Hosted Annual NASA Convention.
June 2019 to	Intern at Barebase studio Bangalore,
March 2020	Attic studio Kochi, Foliage Architects Kochi,
April 2022 to	Evolve Design Studio Bangalore
July 2023	
Aug 2023	DLB Global Bahrain KSA UAE
Present	

EDUCATIONAL BACKGROUND

- 2012 - 13** 10th, St. Marys High School, Cherupuzha.
(Board of Public Examinations, Kerala)
- 2013 - 15** St. Thomas HSS , Kazargod. (Board of Higher
Secondary Education, Kerala).
- 2016 - 21** DC School of Architecture & Design, vagamon.
(Bachelor of Architecture - MG university, Kerala).

SOFTWARES & SKILLS

HAND DRAFTING AND MODEL MAKING	
AUTOCAD	
ADOBE ILLUSTRATOR	
ADOBE PHOTOSHOP	
SKETCHUP	
LUMION	
D5 RENDER	
MS OFFICE SUITE	



Contents.

THESIS.....	06 - 19
A-FRAME.....	20 - 21
COMMERCIAL.....	22 - 27
RESIDENTIAL.....	28 - 35
RECREATIONAL.....	36 - 39
INTERIOR DESIGN.....	40 - 43
INTERIOR FIT-OUT.....	44 - 49
MISCELLANEOUS.....	50 - 51

01 Thesis.

THESIS | ARCHITECTURE

Site Pettamala, Ernakulam, Kerala
Site Area 75 Acres

Introduction.

As human's footprint expands on earth, it results in countless open wounds to the landscape: highly manufactured, altered and deserted land of collapsed ecological system, exposed stones, and little vegetation cover. So, it is very important to restore a destroyed or naturally healing and as part of ecological conservation and education activity. Taking case of a Quarry site itself will be best example to achieve this goal.

Strategy.

Reclaim & Reconnect



Destroyed/ Abandoned quarry



Restoration in Ecological Aspect




Introduction of site specific design intervention


Restoration in Ecological Perspective:

Ecological restoration focuses on repairing the damage human activities have caused to natural ecosystems and seeks to return them to an earlier state or to another state that is closely related to one unaltered by human activities. Ecological restoration is distinguished from the practice of conservation, which is primarily concerned with preventing further losses to ecosystems.

Opportunities in Quarry..

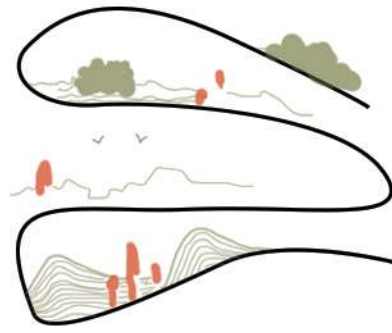

Experience : The peoples experience in spaces are unpredictable but can generate common emotions accordingly.


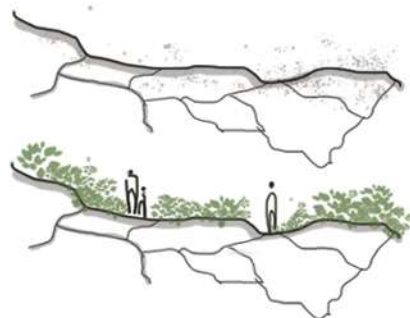


Site Features : Site features merging with the experience creates an emotion among.



..... ? : Merging together the experience and features create something more interactive, profitable and appealing to people and society.

Process.

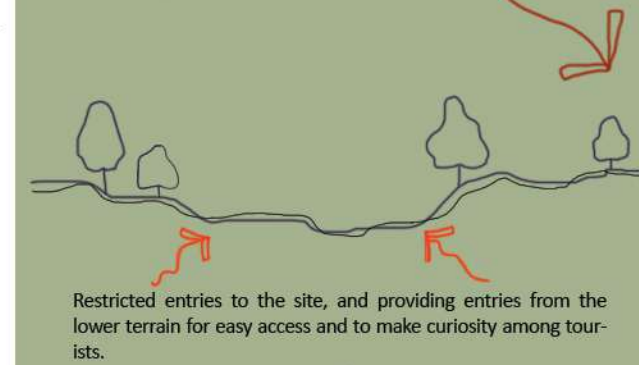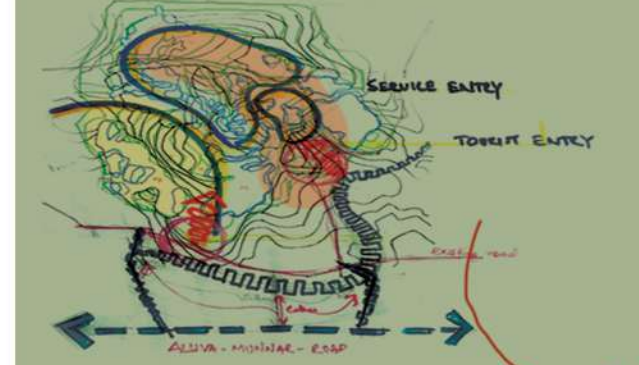

Categorized into adventure & recreational zone and eco resort zone.



Photos taken during site visit



View from the highest point of the site.



View from the lowest point of the site.



Aerial view to the site.



View from the highest points of the site.



View from the lowest point of the site.



View from the lowest point of the site.



Aerial view to the site.

The naturally formed paths create a visually pleasing effect. It has connectivity all over the site and it joins in the middle of the site over a single node.

The site is naturally blessed with scenic beauty and its potential can be well used in the design. The water bodies present in the site and landscape can be maintained and can conserve here. The remaining abandoned land suitable for construction can be modified.

In the middle. Visible from everywhere. And area which has more potential and can remain as its own.

Before it acted as a main magnetic element that attracted tourists, This dangerous point can be a major attraction point of the project.

The highest point in the site can be used as a watchtower which provides a view all along with the site and also an adventure trail/cycle path can be provided for better utilization of the site.

Sensory Analysis.

Key Concept.



- Recreation & Restoration.
- Cultural exchange among tourists.
- Developed economy and living.

Process to Design..

Analyzing opportunities in Quarry and sensory analysis, and then overlaying to get zoning which mainly leads to the design process here.

Also with the site features humans emotions are overlayed and taking it as the main key concept.

Excitement

First time visiting the quarry excites us as we have no clue of the place.




Curiosity

From the highest point, visitors will be coming down where the astonishing beauty welcomes.

Calmness/Peace

Water bodies, existing vegetation, and natural quarry wall separation, and beautiful landscapes give an ambient and tranquil state of mind.

Zoning.

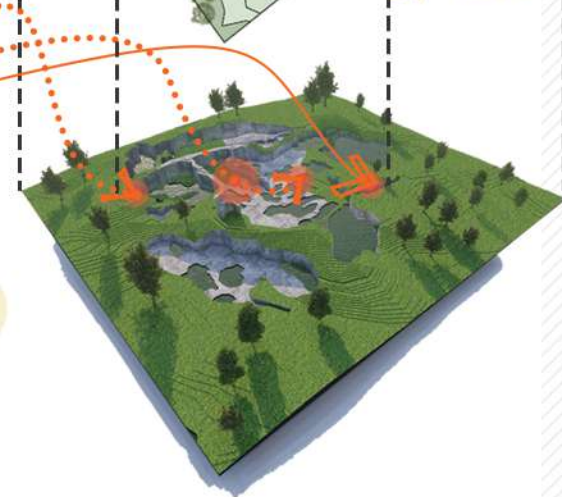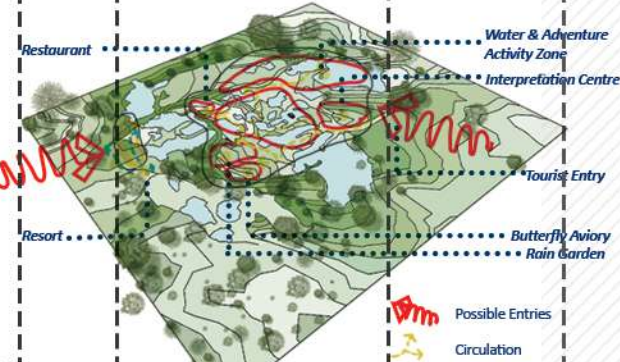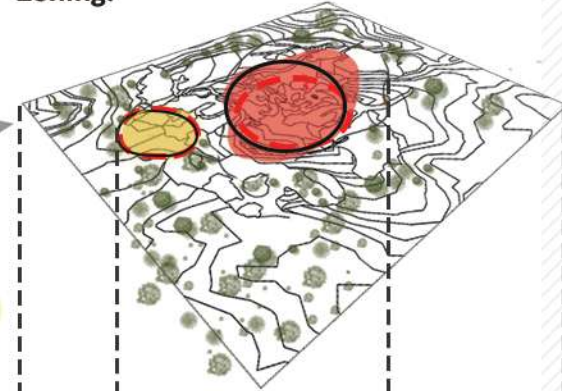

Depth

Small and Large quarry Pits

Hard rocky quarry



1. Parking
2. Tourist entry & Admin Block
3. Interpretation Centre
4. Buggy Parking
5. Rain Garden
6. Butterfly Aviary
7. Seating space
8. Amphitheatre
9. Toilet
10. Kiosks - (2)
11. Viewing Deck.
12. Restaurant
13. Activity Space
14. Experiential paths


15. Childrens play area
16. Adventure admin
17. Staff parking
18. Water activity & Extended deck space
19. Trekking path
20. View point + recreational
21. Rock climbing, water jumping etc..
22. Bicycle path & parking
23. Sky trail
24. Staff Accomodation
25. Water tank
26. Waste management
27. Water treatment
28. Resort

- Build Form
- Pathway
- Existing Road
- View Decks
- Sky Trail
- Parking
- Landscape
- Waterbody



- Tourist Entry
- Service Entry
- Resort Entry


Adventure admin.

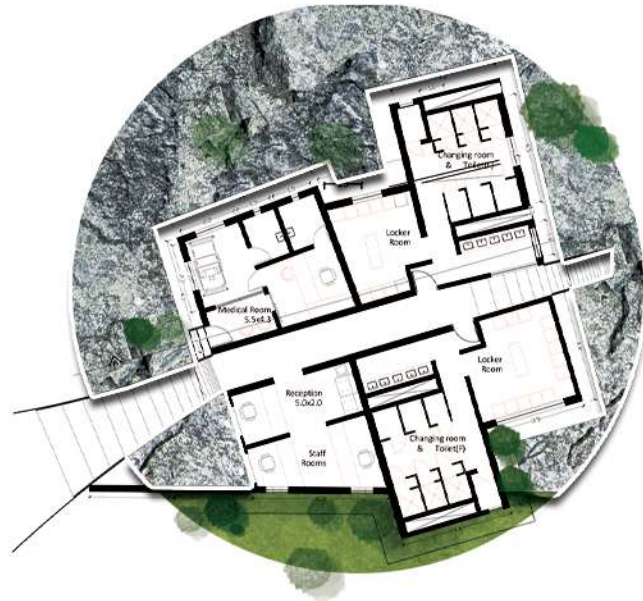

Plan

Low-risk and other adventure & water-based activities provided make the visit of tourists more interesting. And tempt to stay at the cottages for a day after all these activities and a day spent. Every path and space in the design is emotionally connected with people's minds which gives a pleasing mind.

Visitors entry & Admin.

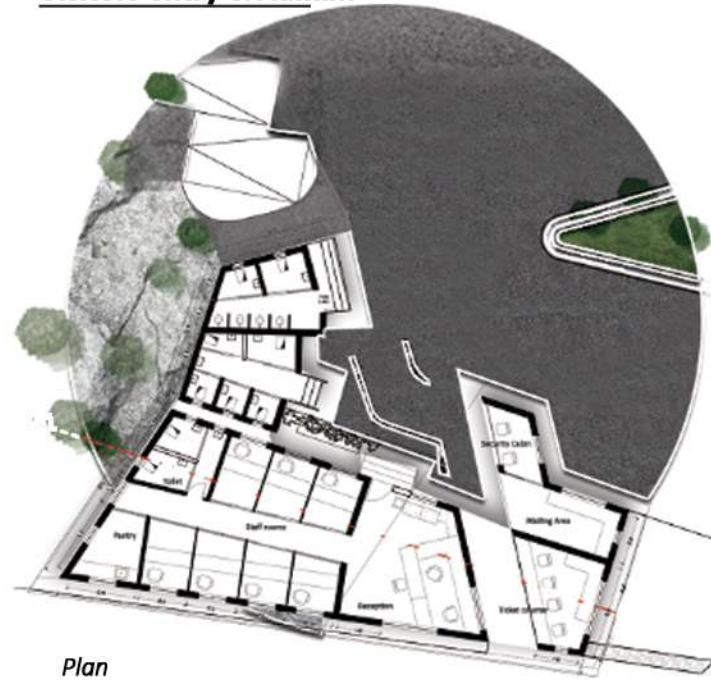


Plan

In the adventure zone mainly activities are incorporated like deep water jumping, trucking, kayaking, hill climbing, etc.. And in the water zone, two quarry pits are connected to make a large zone for water-based activities and boating.




Spatial distribution is done with visitors' experience connecting with their emotions and needs. From drop-off, visitors will be entering the admin block consisting of a ticket counter and waiting area in the public zone.

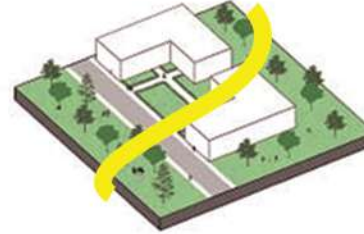


Adventure admin block is designed in between the recreational natural trail zone and water & adventure zone. It acts as a transition & connecting space in between, with facilities provided like, locker n changing rooms, restrooms, etc..



Recreational and seating spaces are given in between the zones as eco park. So that visitors won't get bored of walking from one place to another. And also, the entire site is designed in such a way as people could experience it to the fullest.

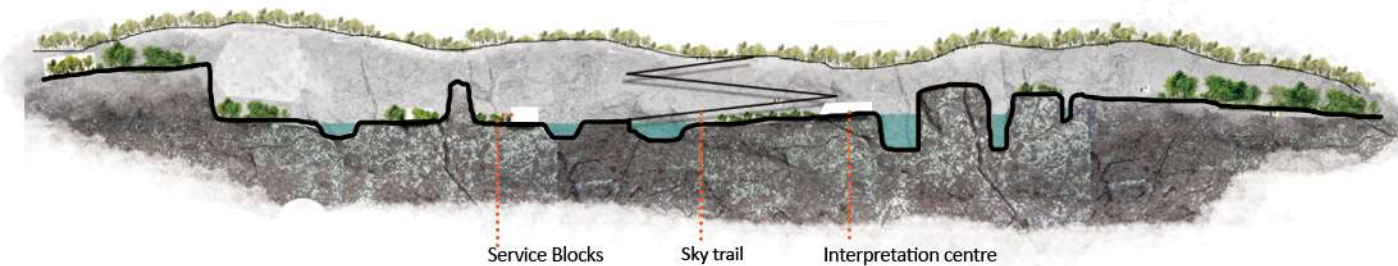


Site Section AA'

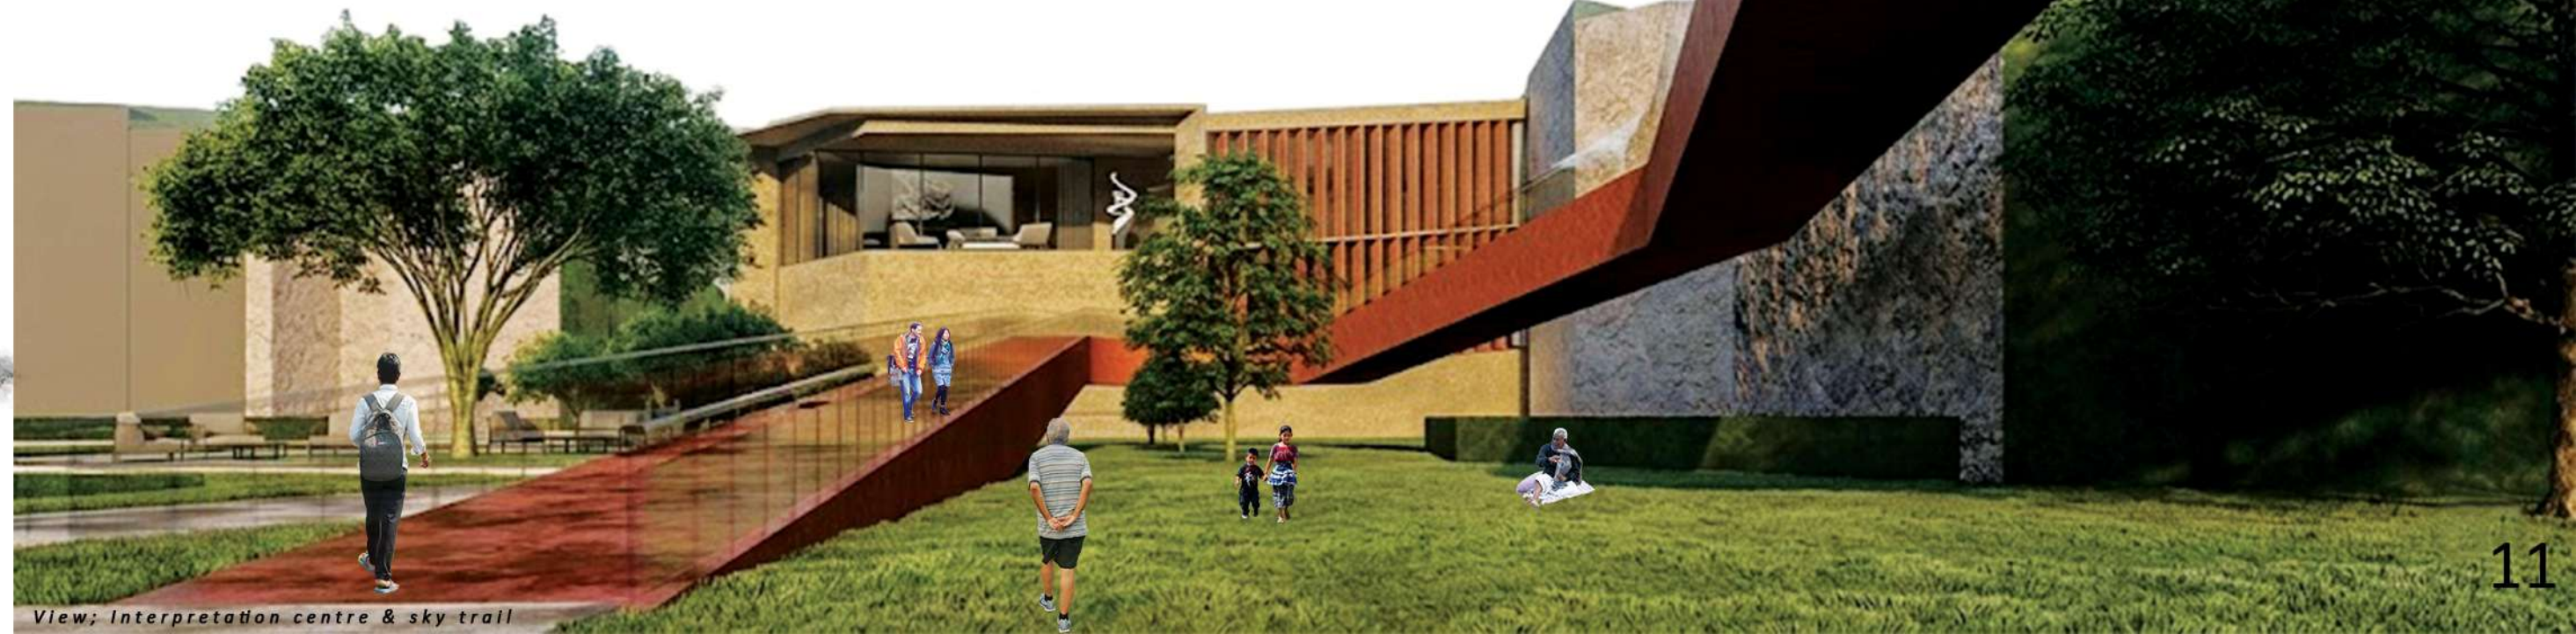

View; Interpretation centre & sky trail


Interpretation Centre.

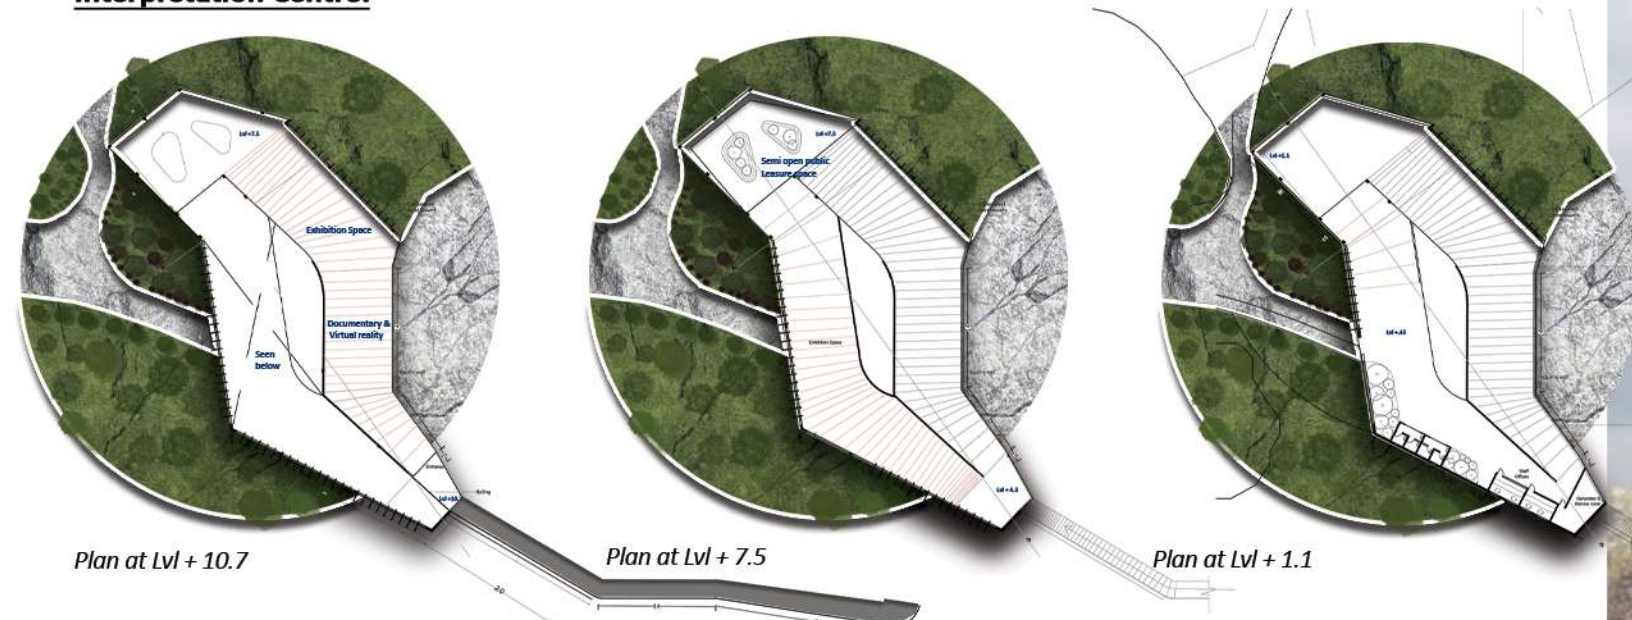

From drop off (lvl +13m) people are taken down through an interpretation center that explains the past, and present of quarry through exhibitions and VR experience. An open mesh up to the interpretation center is given which gives a partial view to the other part that creates enthusiasm among visitors.


One side of the interpretation center has remained with the quarry wall itself which gives a serene experience and the true texture along with sound effects and the play of light and shadow from the exterior corten steel facade gives a serene experience.

Also, the main vision of the project itself was to bring awareness among local and tourist people. So this center while walking through directly explains the scenario of quarry in past and how quarrying has manipulated the site and its ecology and finally how can we conserve and contribute to bring back and restore the past glory. So before entering, the visitors will get the whole idea of the project and the need for conservation.

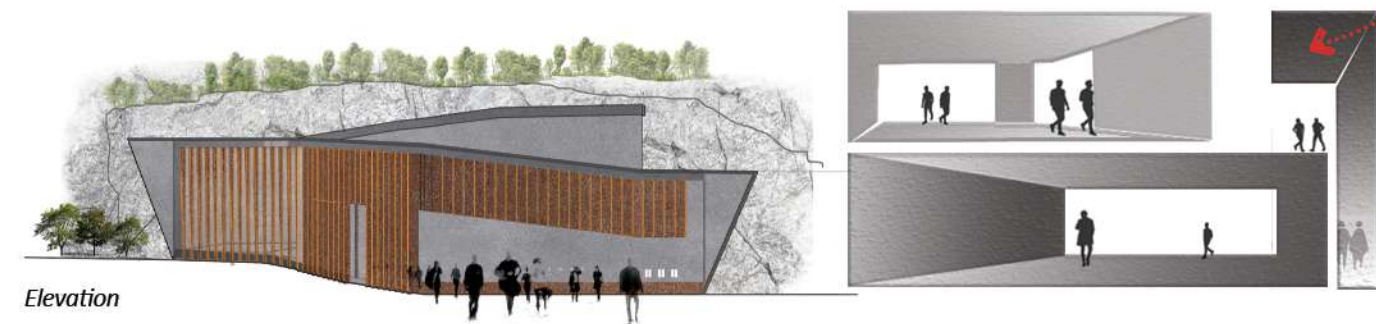

View; Interpretation centre & sky trail

Butterfly AViory

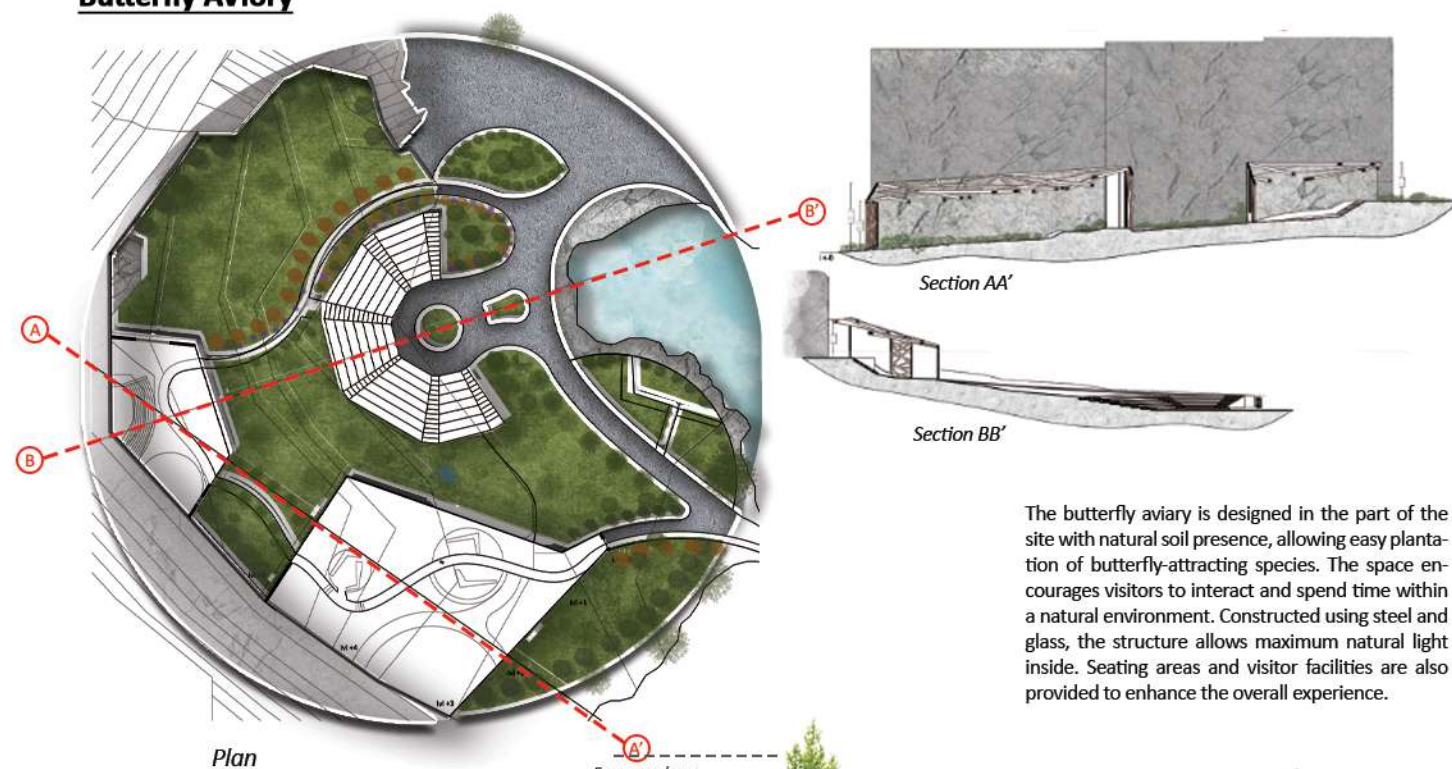

Plan


A rain garden is designed around the aviary to allow rainwater to naturally percolate into the ground. Native plant species are used to improve water quality, provide localized flood control, and create an aesthetically pleasing landscape. The garden also supports diverse planting opportunities while contributing to natural water purification.

The butterfly aviary is designed in the part of the site with natural soil presence, allowing easy plantation of butterfly-attracting species. The space encourages visitors to interact and spend time within a natural environment. Constructed using steel and glass, the structure allows maximum natural light inside. Seating areas and visitor facilities are also provided to enhance the overall experience.



View: Butterfly AViory

SKY TRAIL.

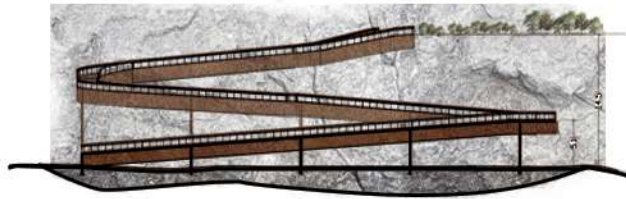


At the end of the trekking path in the adventure zone, a viewing deck with seating spaces is provided at the highest point of the quarry, approximately 35–40 meters above. Designed as a resting point after the long trail, it offers panoramic views of the entire quarry, creating a unique and immersive experience for visitors.



At the end of the journey, visitors from both the adventure and recreational zones exit through a sky trail that connects directly to the parking area above.




Giving different entry and exit gives more opportunity for the users to experience the well. And gives an overall view.

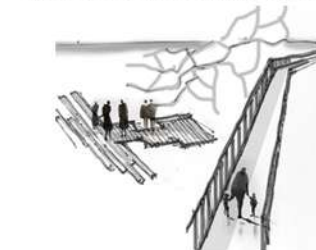


View; Sky Trail

Resort

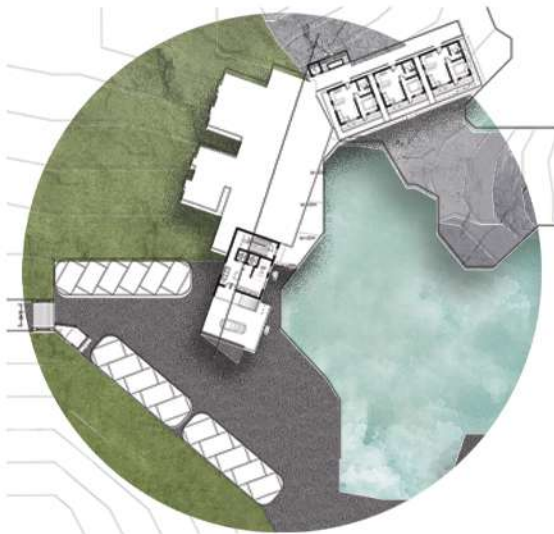

Plan at Lvl +20.8 M
Not to scale

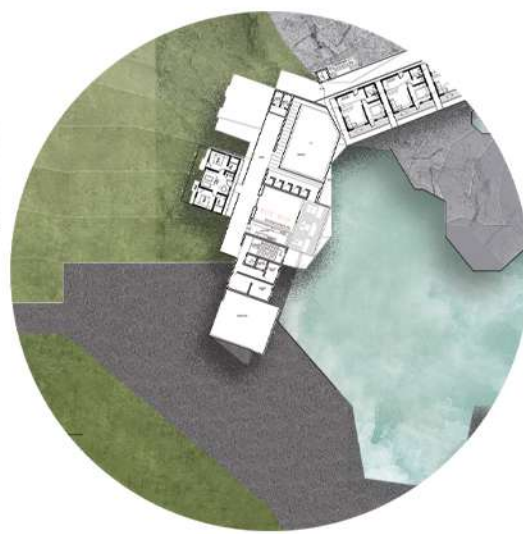

Plan at Lvl +23.8 M
Not to scale



Plan at Lvl +26.8 M
Not to scale

The visitor accommodation is located on the quieter side of the quarry, offering panoramic views and privacy from other activities within the site. Planned along the north-south axis, the development is arranged across multiple levels to maximize views while minimizing site alteration through controlled cutting and filling.

A reception and waiting lounge are provided at the drop-off point, with lifts and staircases connecting visitors to different levels. The design includes two types of cottages, an amphitheater, infinity pool, and restaurant spaces. Extended balconies and viewing decks are oriented toward the quarry to fully utilize the surrounding landscape, while a steel bridge connects different parts of the development.




02 A Frame Cabin House.

RESIDENTIAL | ARCHITECTURE

Client Jobin Joseph
Site Alakode- Kannur, Kerala
Built Area 1435 sq.ft

Client Requirement.

Designed as a contemporary A-frame cottage nestled within the hilly landscape of rural Kannur, the project responds sensitively to the steep sloping terrain while embracing the natural surroundings. The primary challenge was to integrate the client's spatial requirements within the difficult topography, achieving a balance between functionality, structural feasibility, and minimal site intervention.

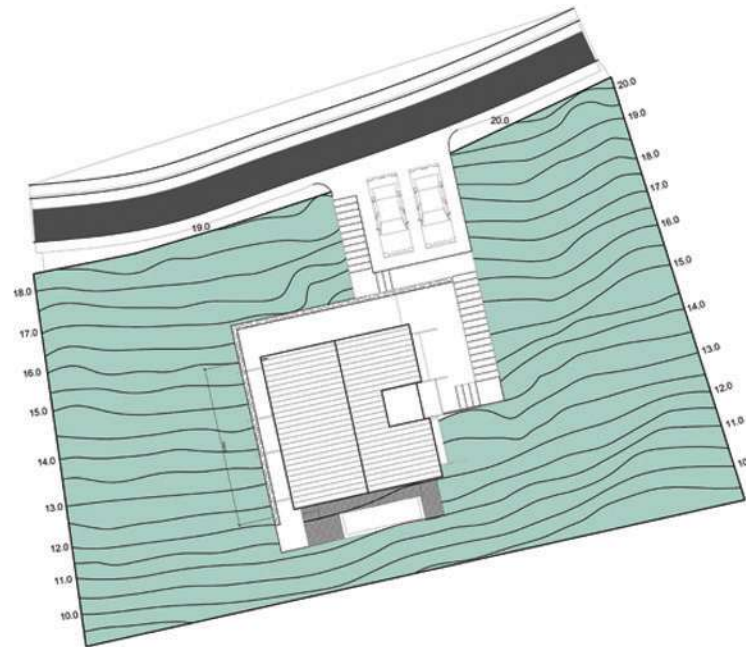

SITE LAYOUT



GROUND FLOOR PLAN



FIRST FLOOR PLAN

Area GF - 810 sqft
Area FF - 615 sqft
Total Area - 1425 sqft



03

Commercial Design.

- CLIENT | AVINASH BYRATI | WEST SIDE GROUP


Introduction.

Commercial design for Avinash group to lend out for TATA's clothing brand west side.


Strategy & Concept.

The design follows a typical West-side group pattern while incorporating subtle elements of our design approach. The proposal focuses on adapting to the client's requirements through a user-friendly layout with maximum display-oriented spaces.




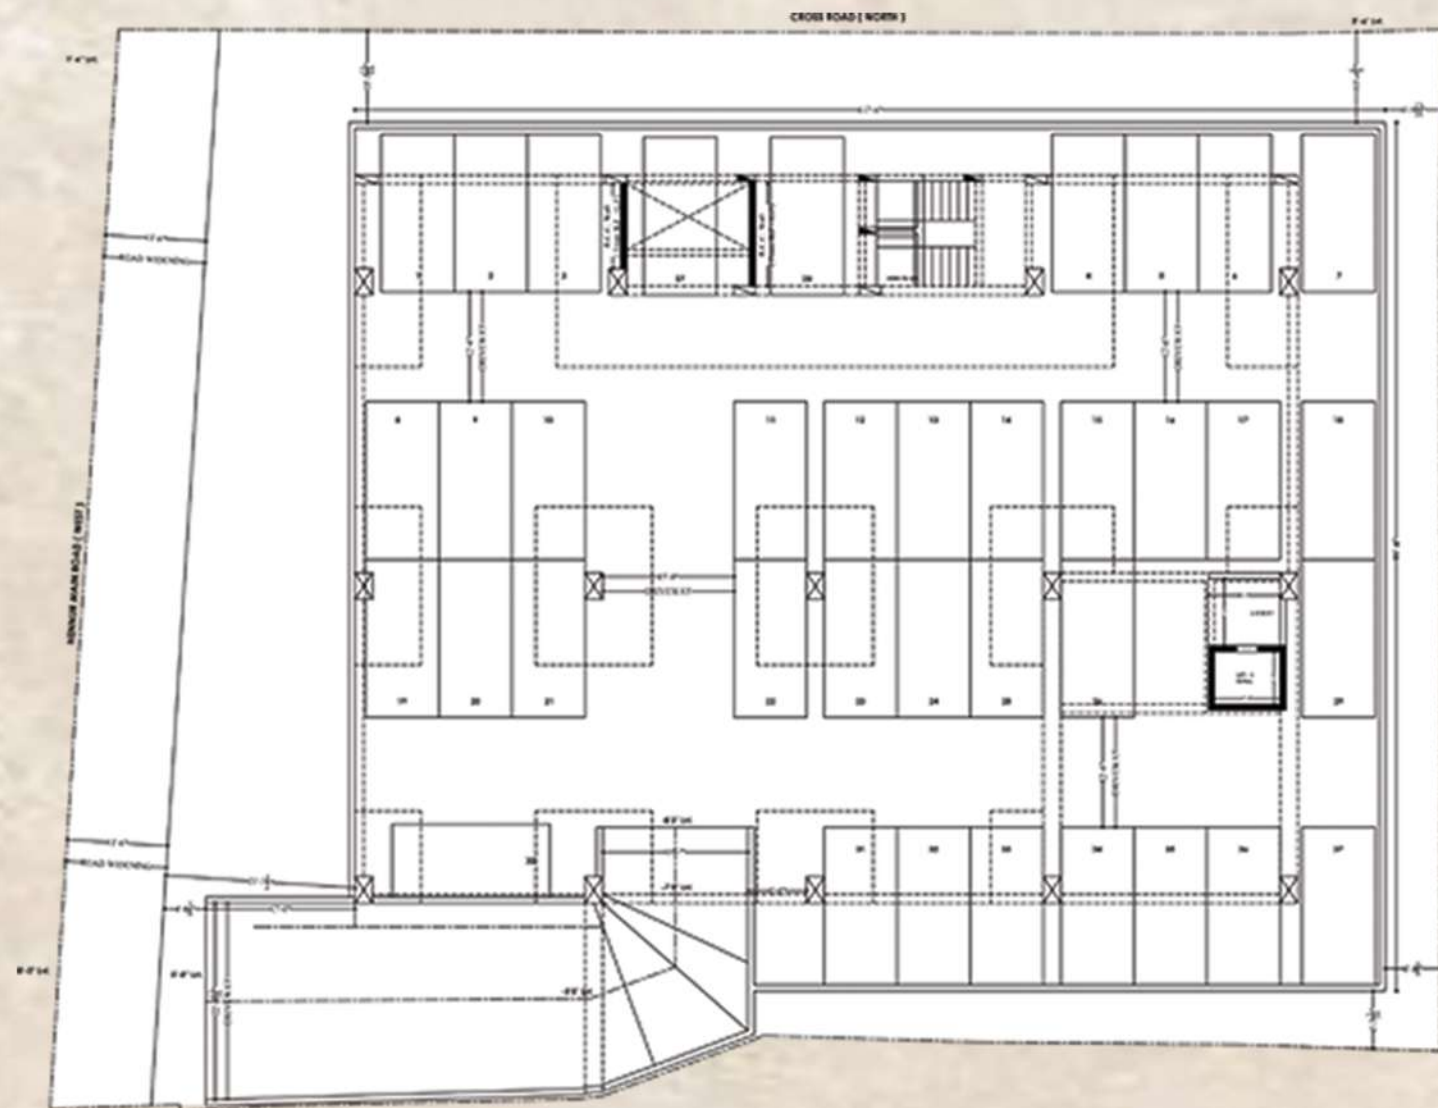


Basement Floor

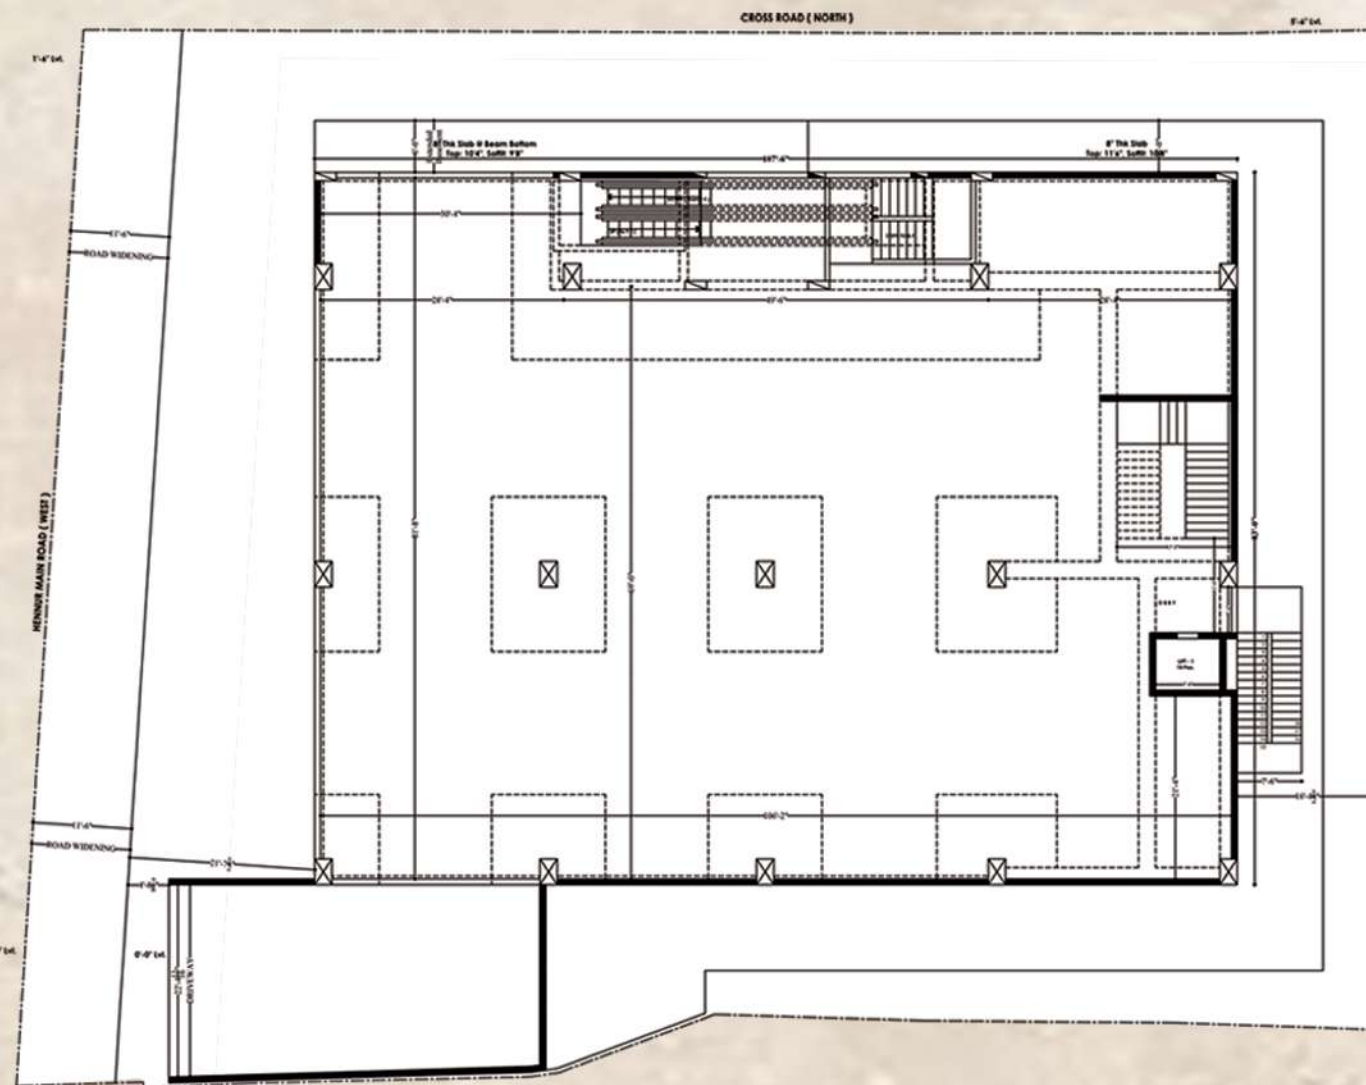

Typical Floor Plans (Ground & First)

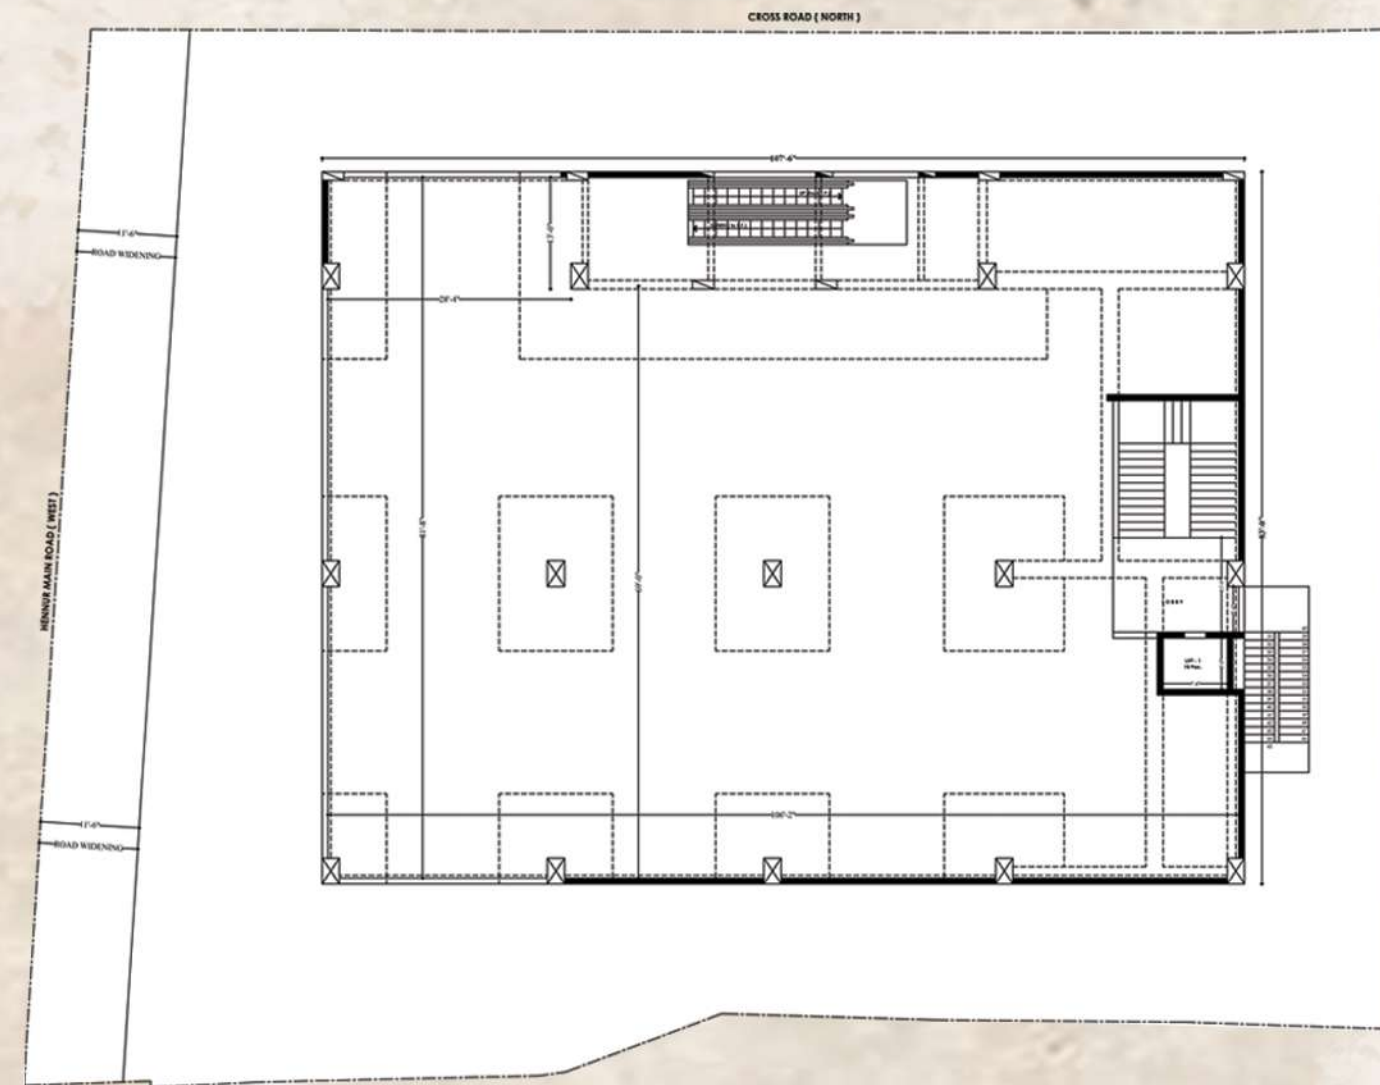

Terrace Floor

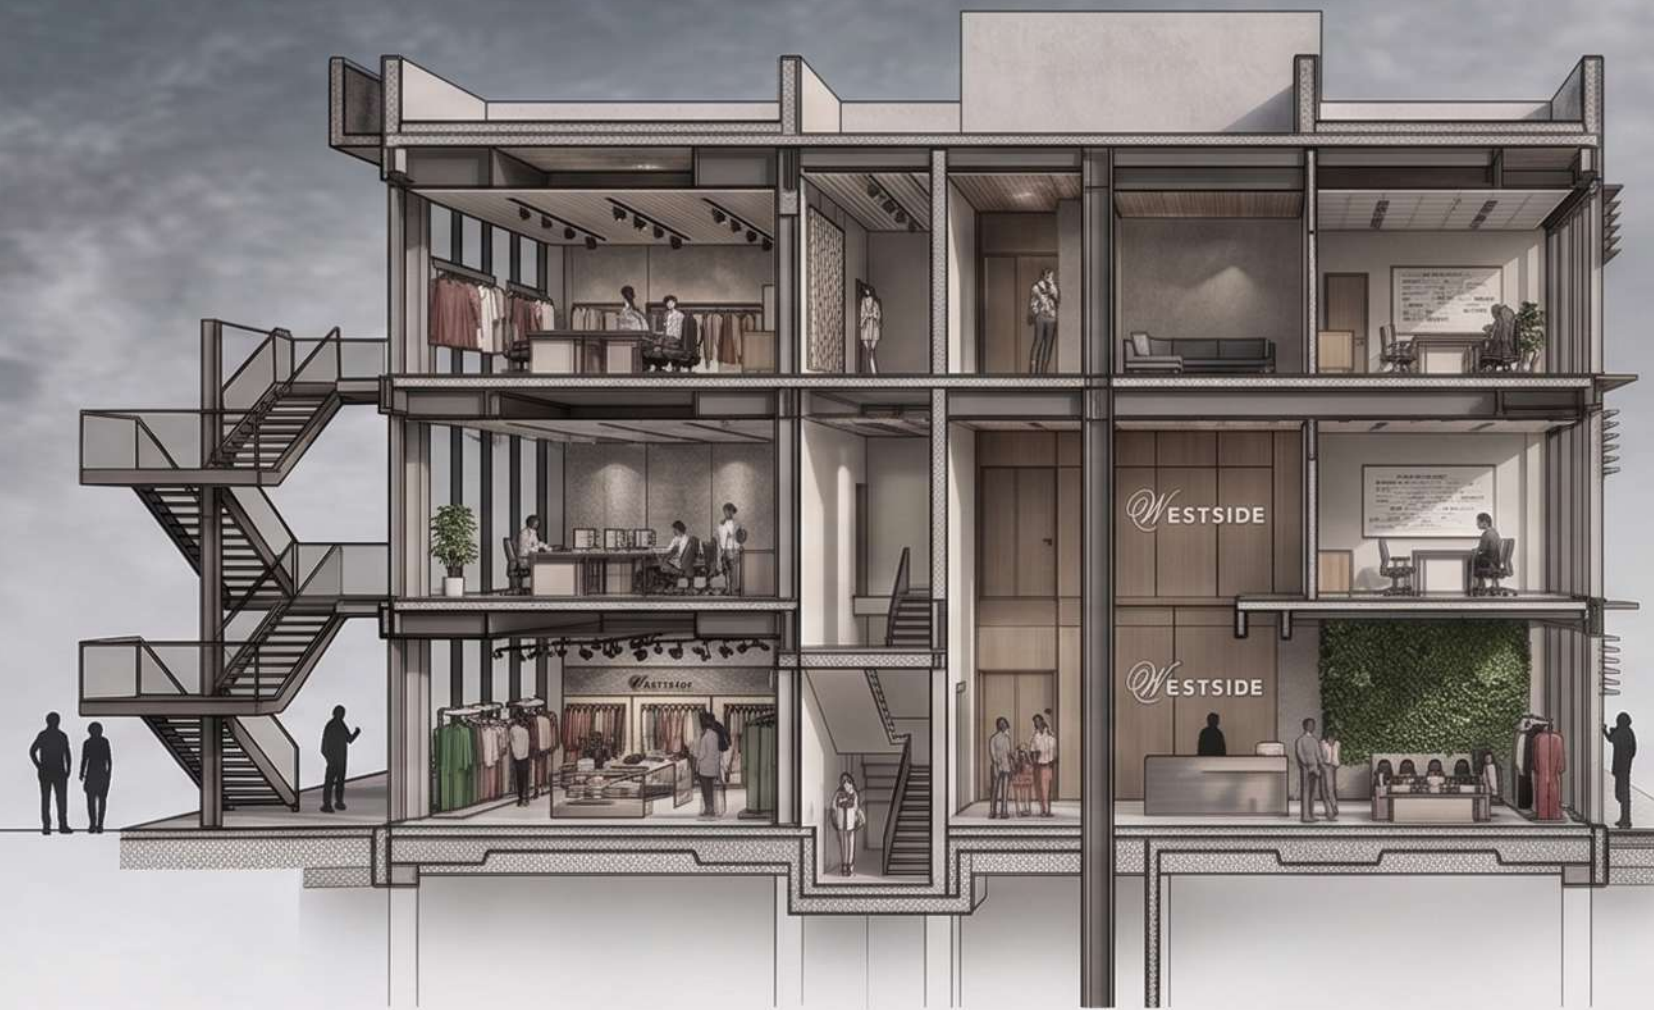

Section



Front Elevation

Side Elevation

04 Residential Design.

- CLIENT | RAVINDRANATH


Introduction.

A residence designed for a businessman in Bangalore, featuring four bedrooms, formal and family living areas, a common study space, and a dedicated home theatre. The design focuses on comfort, functionality, and contemporary living.


Strategy & Concept.

Privacy and maximum space utilization were the primary concerns of the client, which were carefully incorporated into the design. Along with this, interactive spaces were created to encourage connection and discussion among family members.




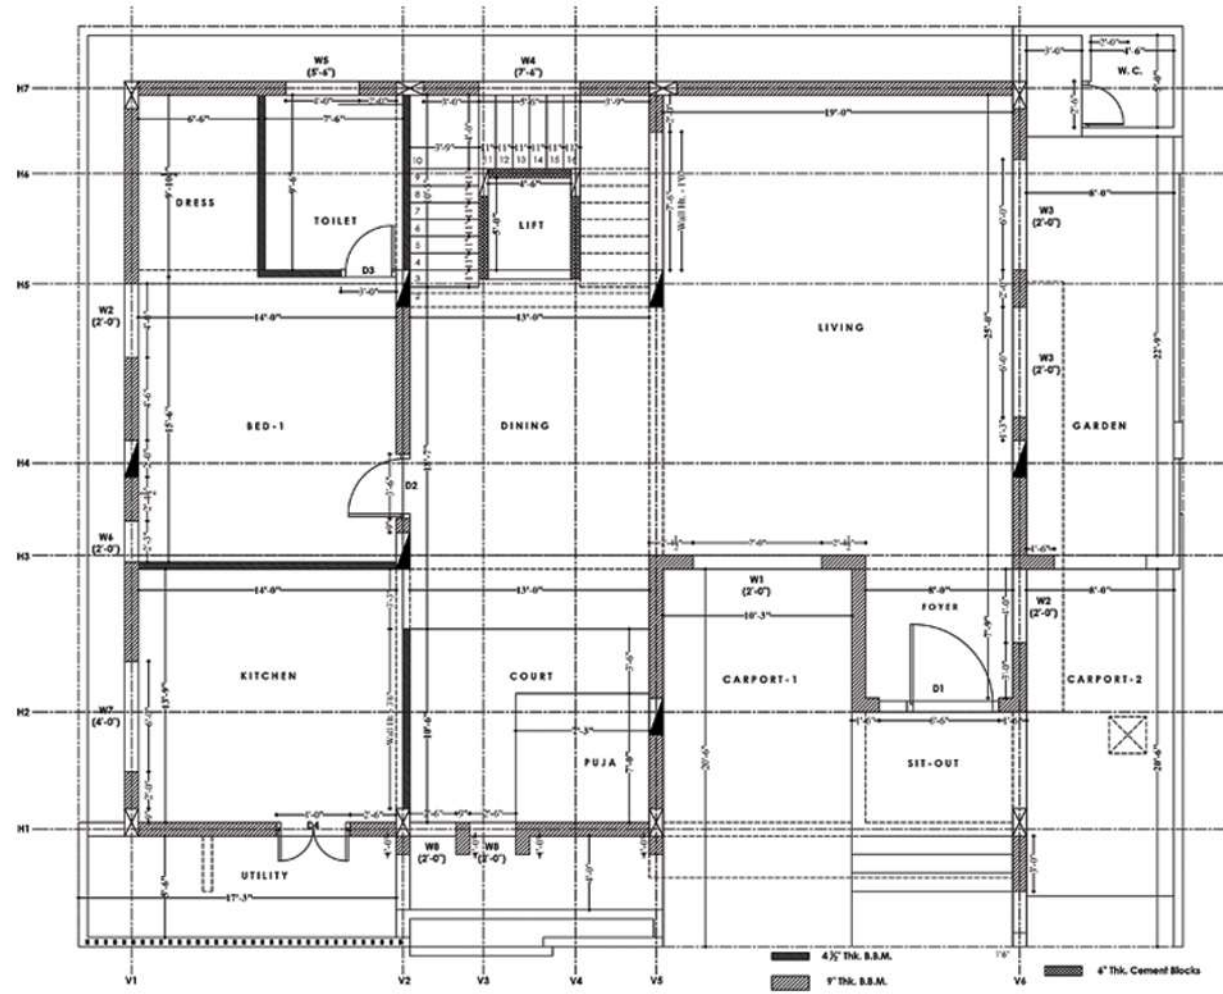


Ground Floor

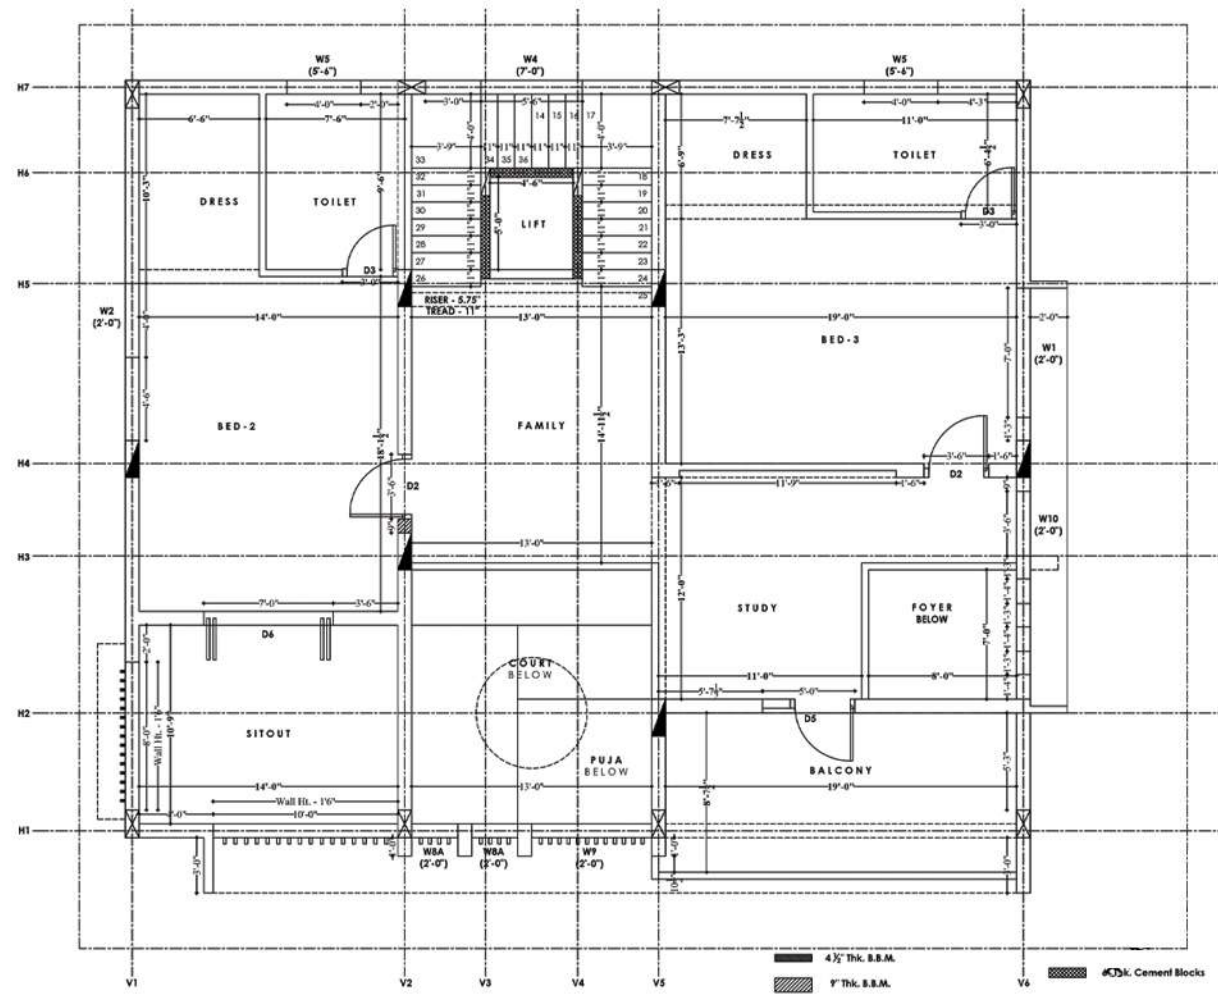


First Floor

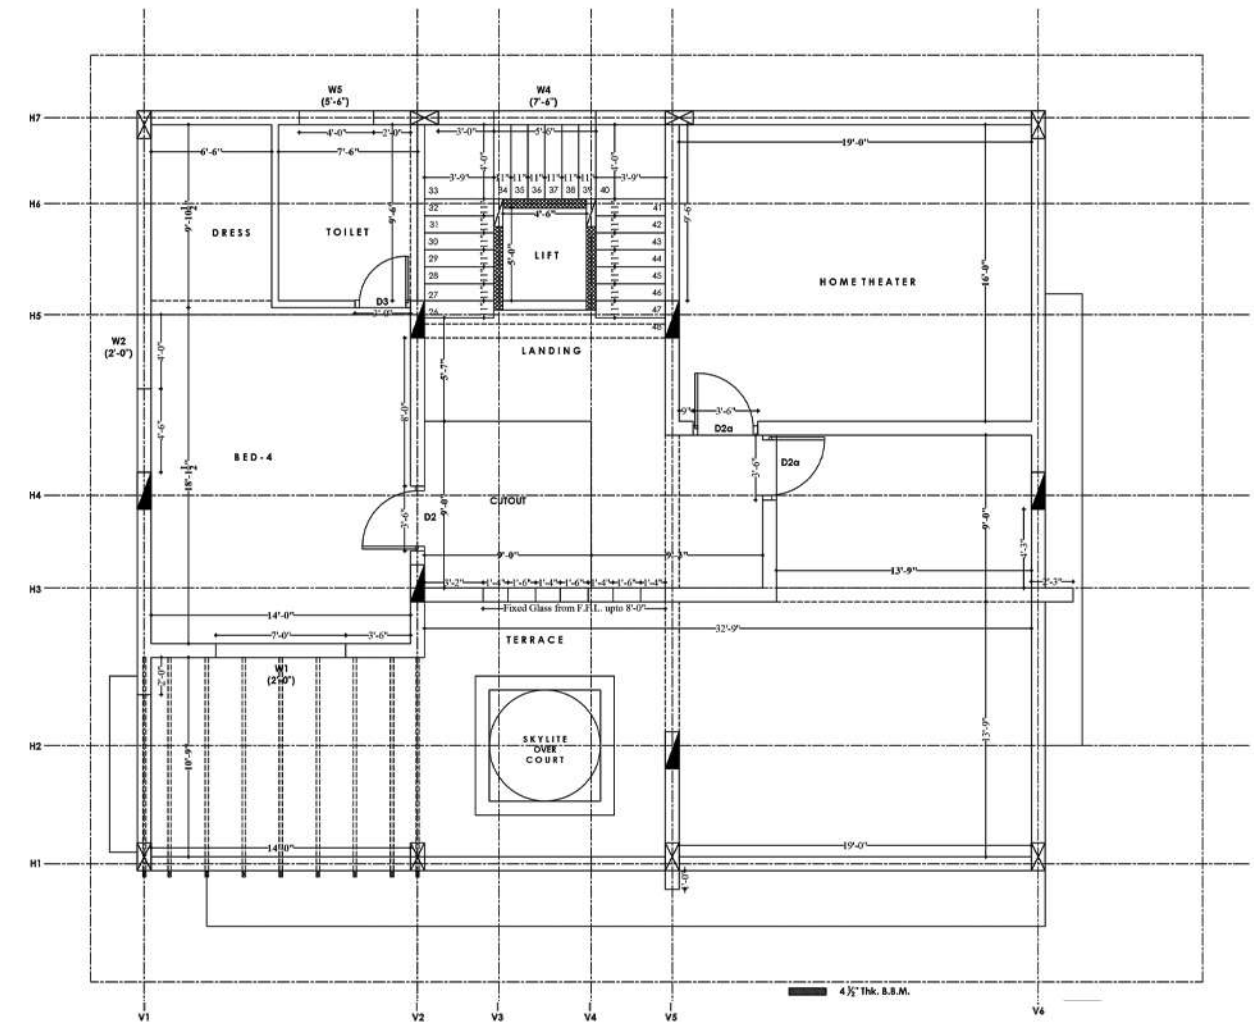


Second Floor

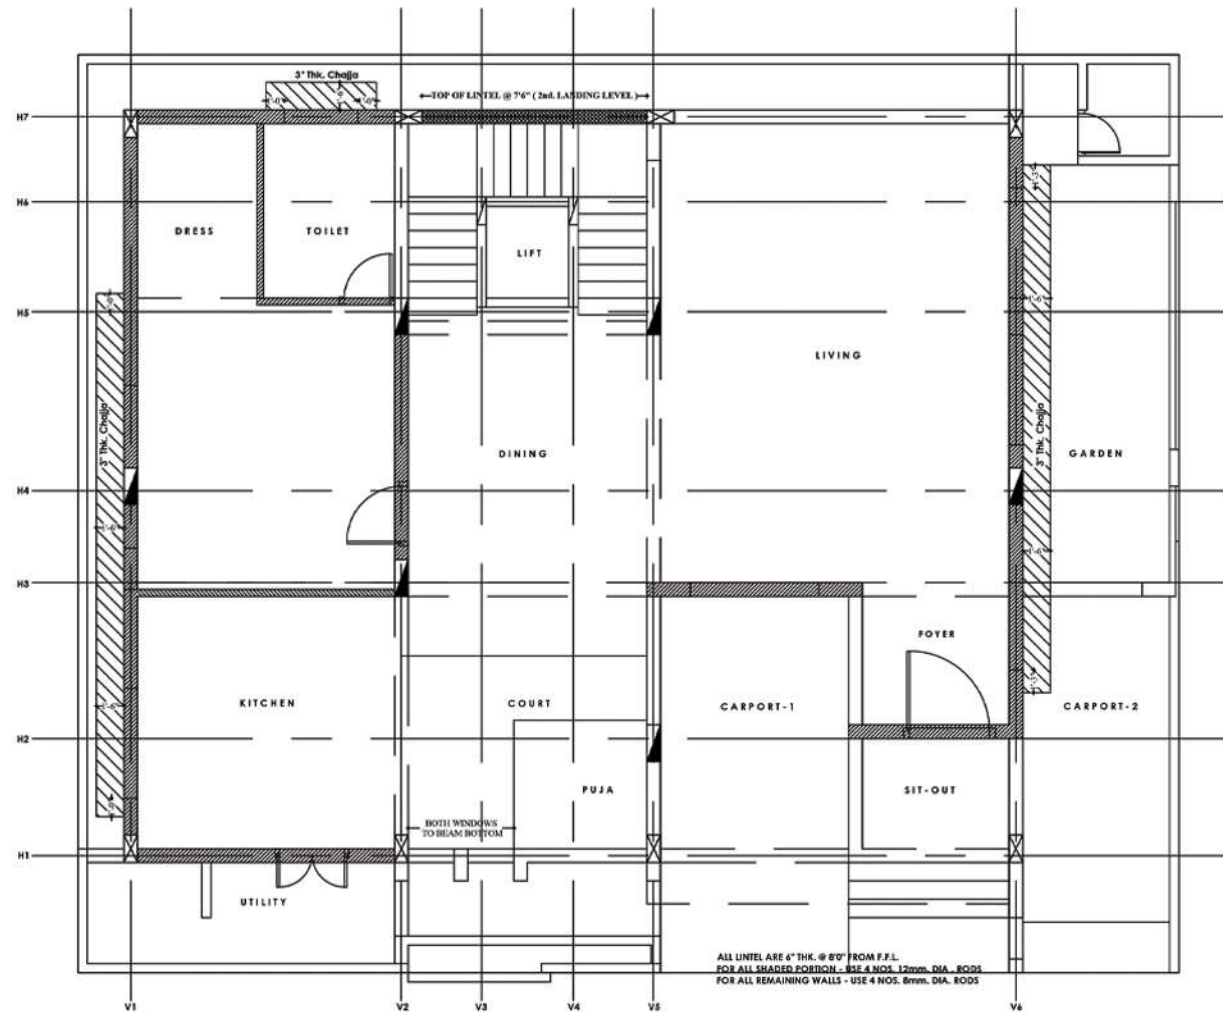

Lintel Drawing

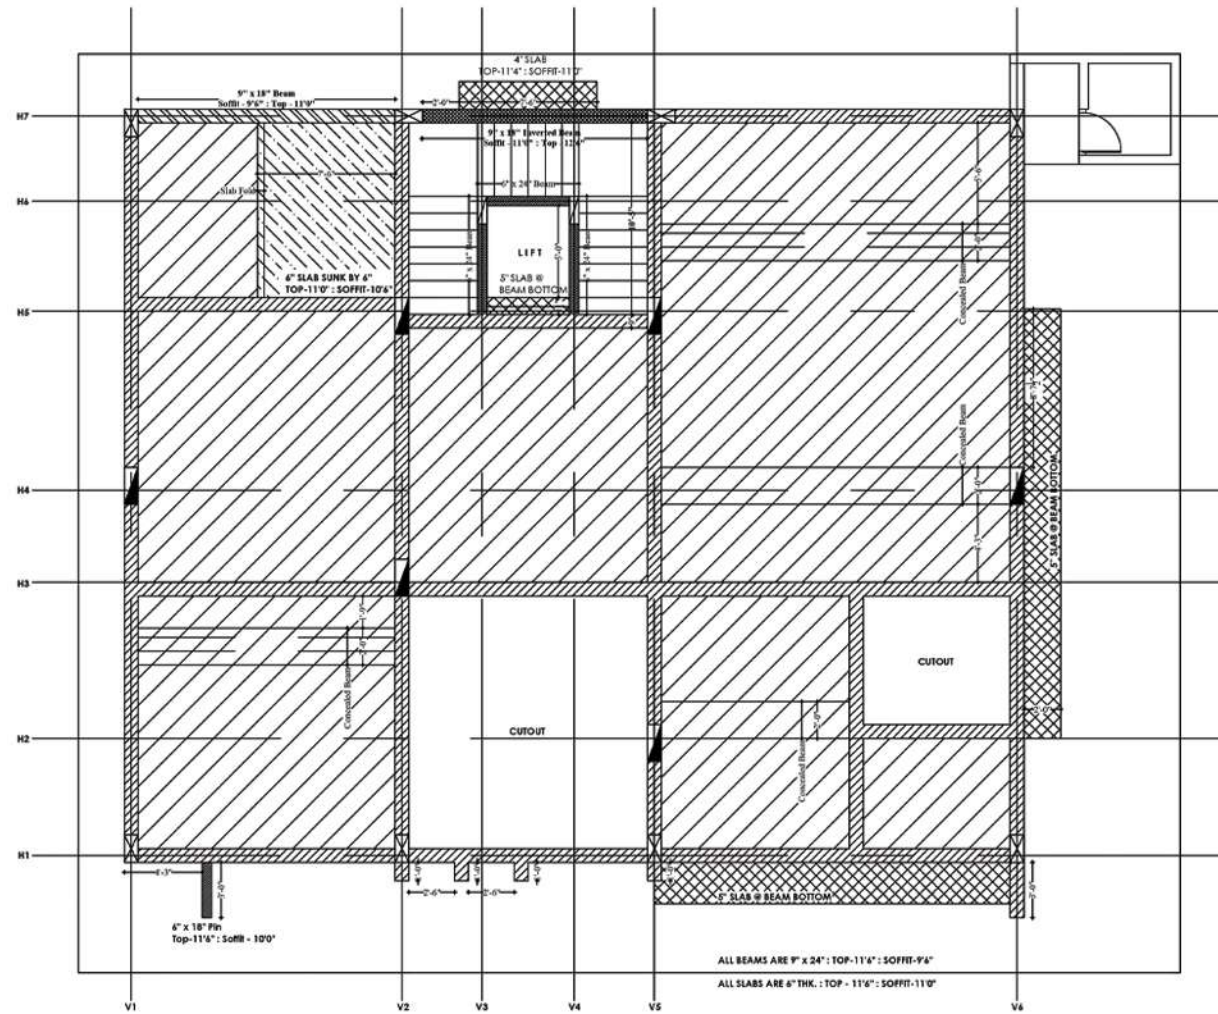

Slab Drawing

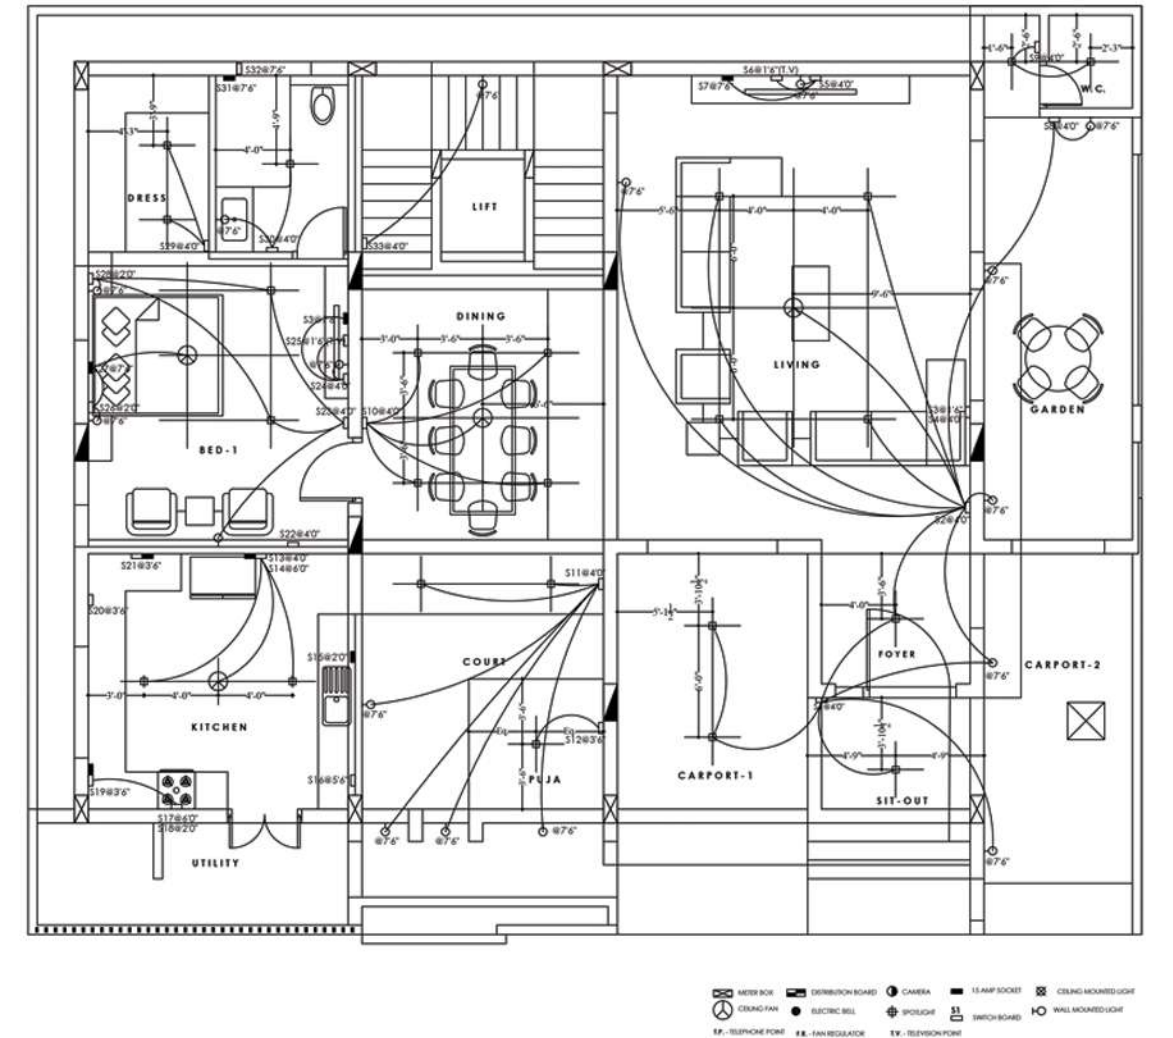

Electrical Drawing

05 Resort Design.

RECREATIONAL | ARCHITECTURE


Site Kaginhare | Bangalore | Karnataka

Introduction.


A resort designed in Kaginhare on the outskirts of Bangalore, where working with the natural contours became both a creative challenge and an engaging problem-solving process. The design focuses on minimizing intervention to the existing topography while preserving the natural character of the site.

Strategy & Concept.


The resort proposal demonstrates how architecture can coexist with challenging terrain while preserving the authenticity of the site. By respecting the contours and integrating natural elements into the planning process, the project creates a sustainable and experiential destination rooted in its landscape context.

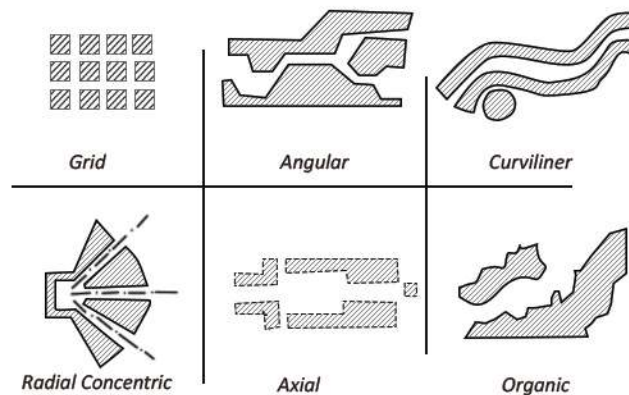

For the contoured site, a mixed-use planning approach was adopted by combining different architectural patterns and layouts that best respond to the natural terrain and site conditions.

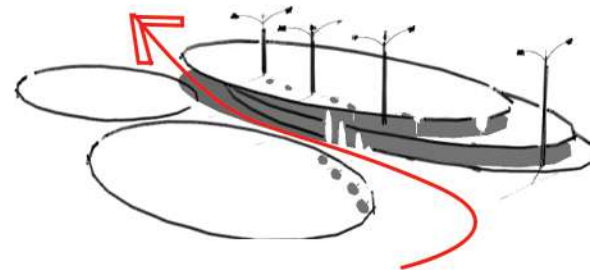

Pathways of experience in between

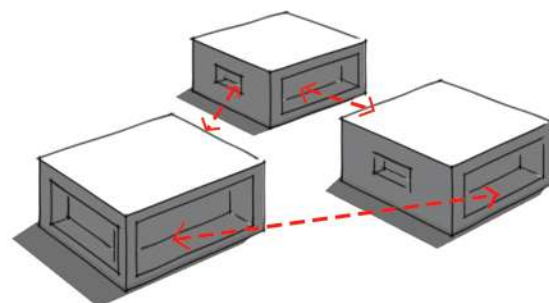

Design maintaining visual connectivity.





The private zone consists of single cottages designed to ensure maximum privacy. Buffered by existing trees on one side, the cottages are planned to provide guests with a secluded and comfortable space to relax and enjoy the surroundings.

This part of the site, located near the stream in the lower contour, is designed as a recreational zone featuring an infinity pool and an open dance deck.

The second set of cottages completely focus on view to the river flowing through the valley. It has four set of rooms which lies in two different floors.

The cottages with shared balconies and cluster rooms are also focusing on view and can be utilized for a group of people coming together.

- Public zone which includes restaurant and recreational activity spaces such as play area and activity space also the service zone and reception and welcome desk is designed here.

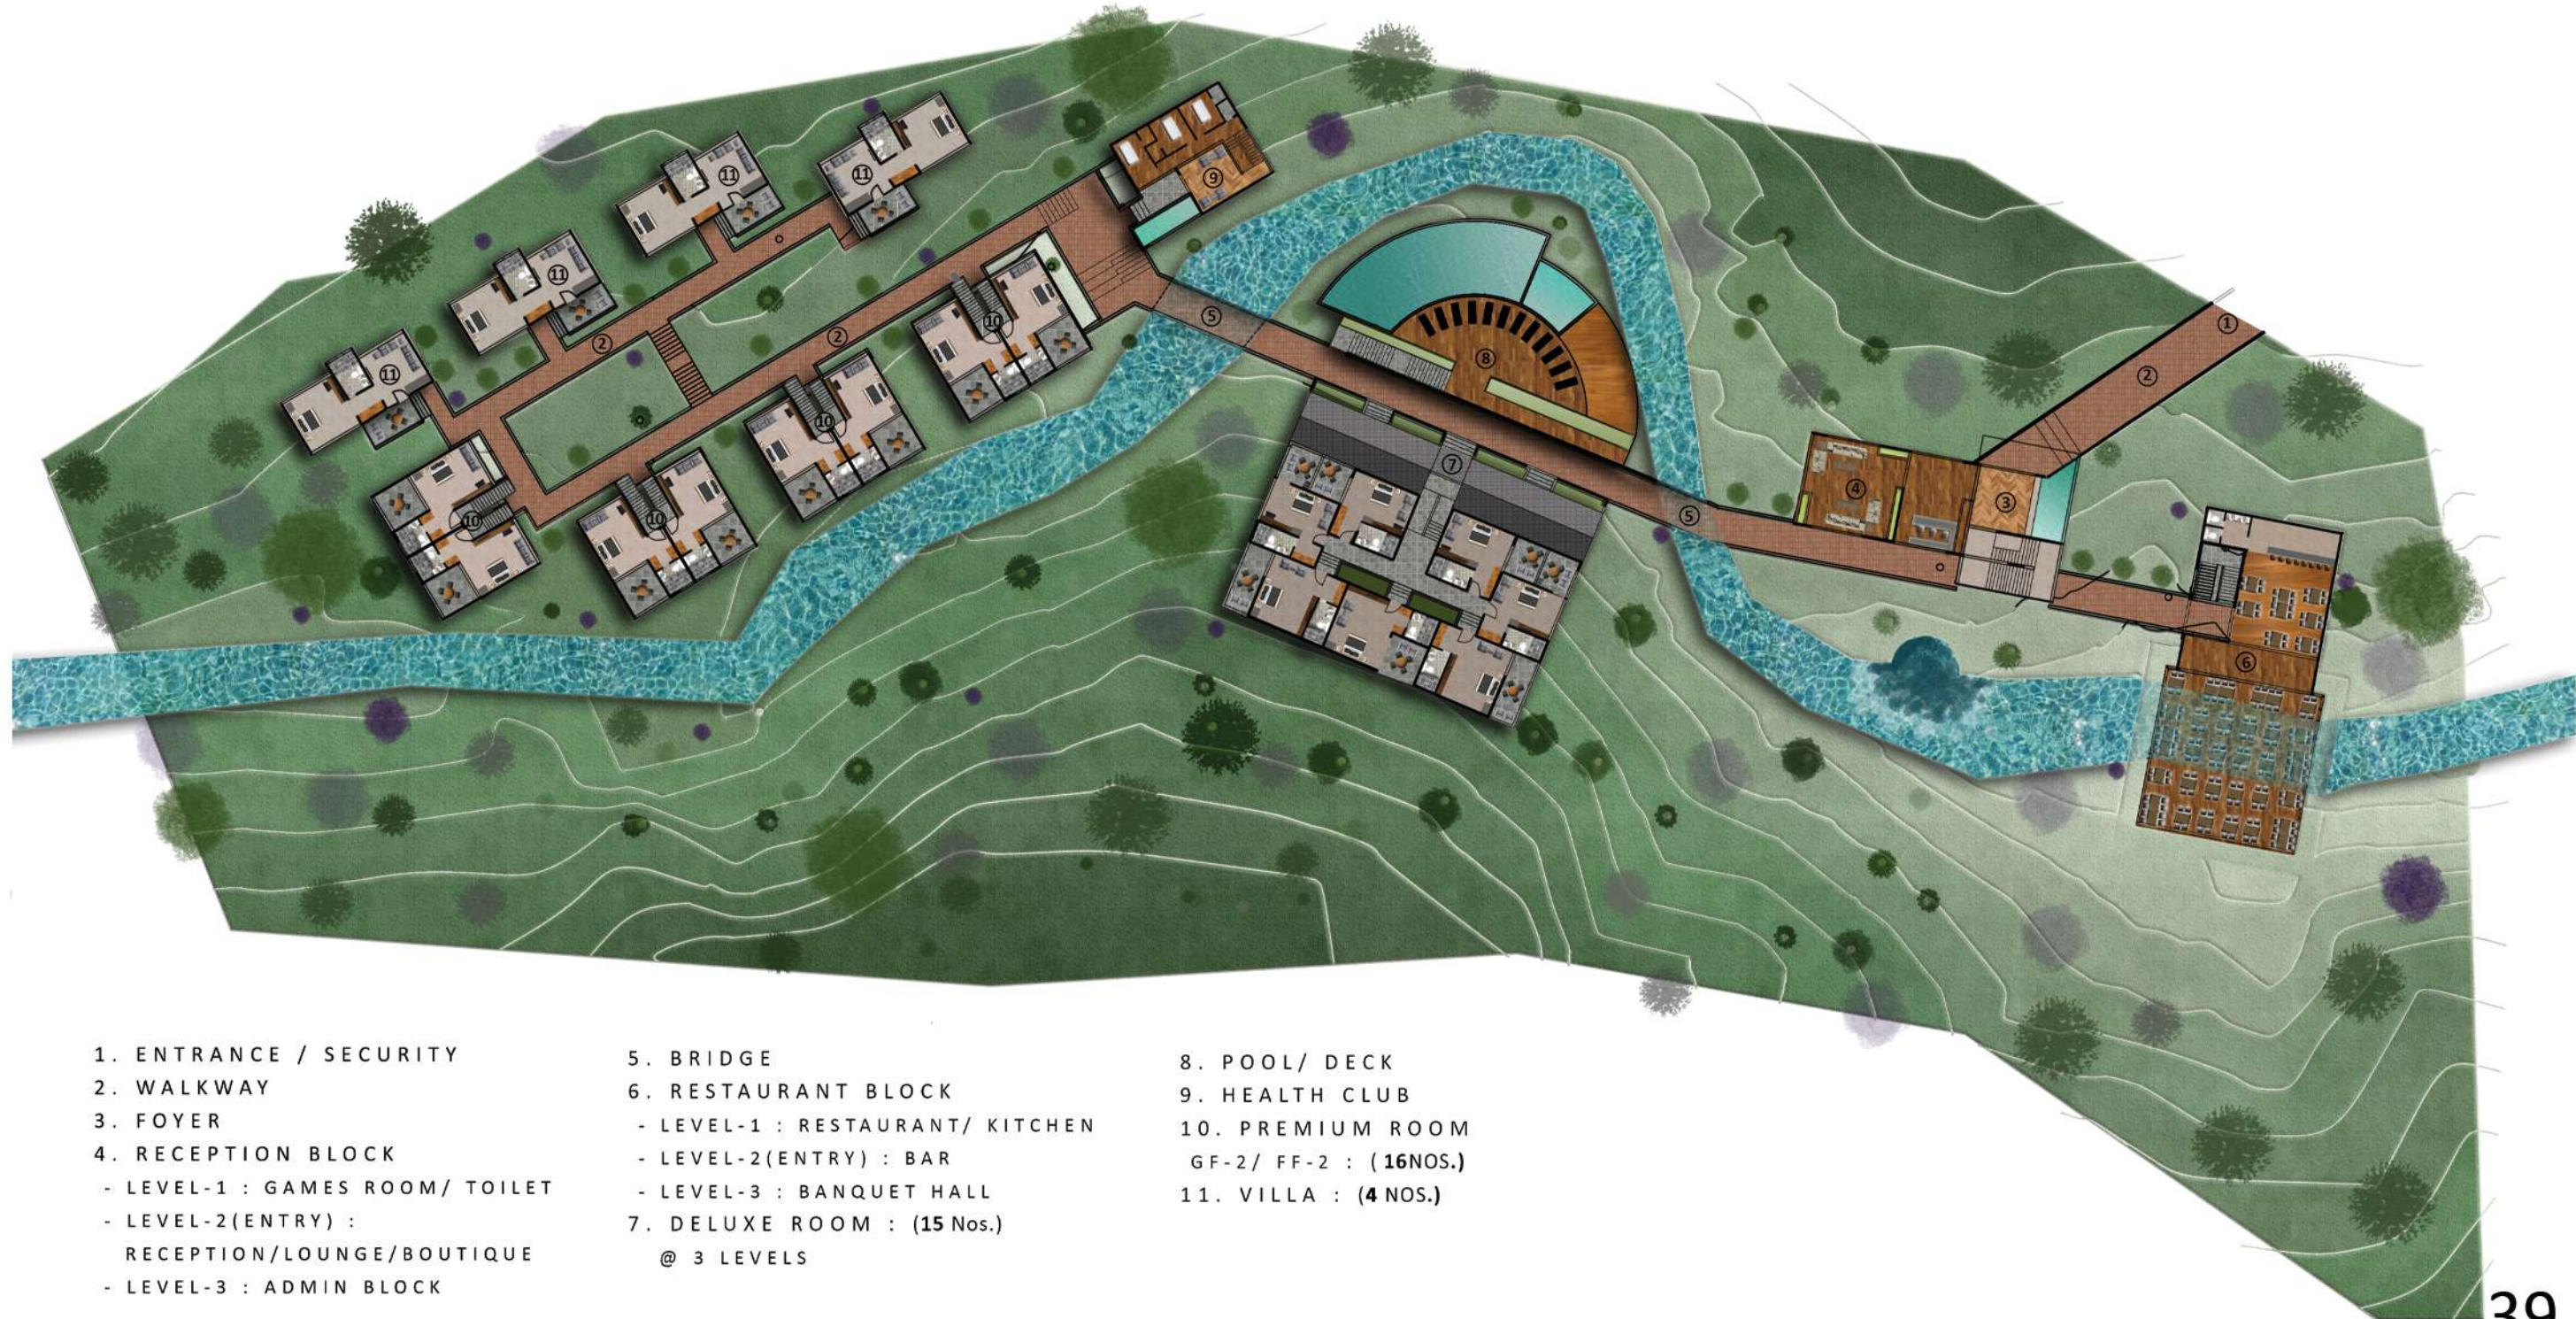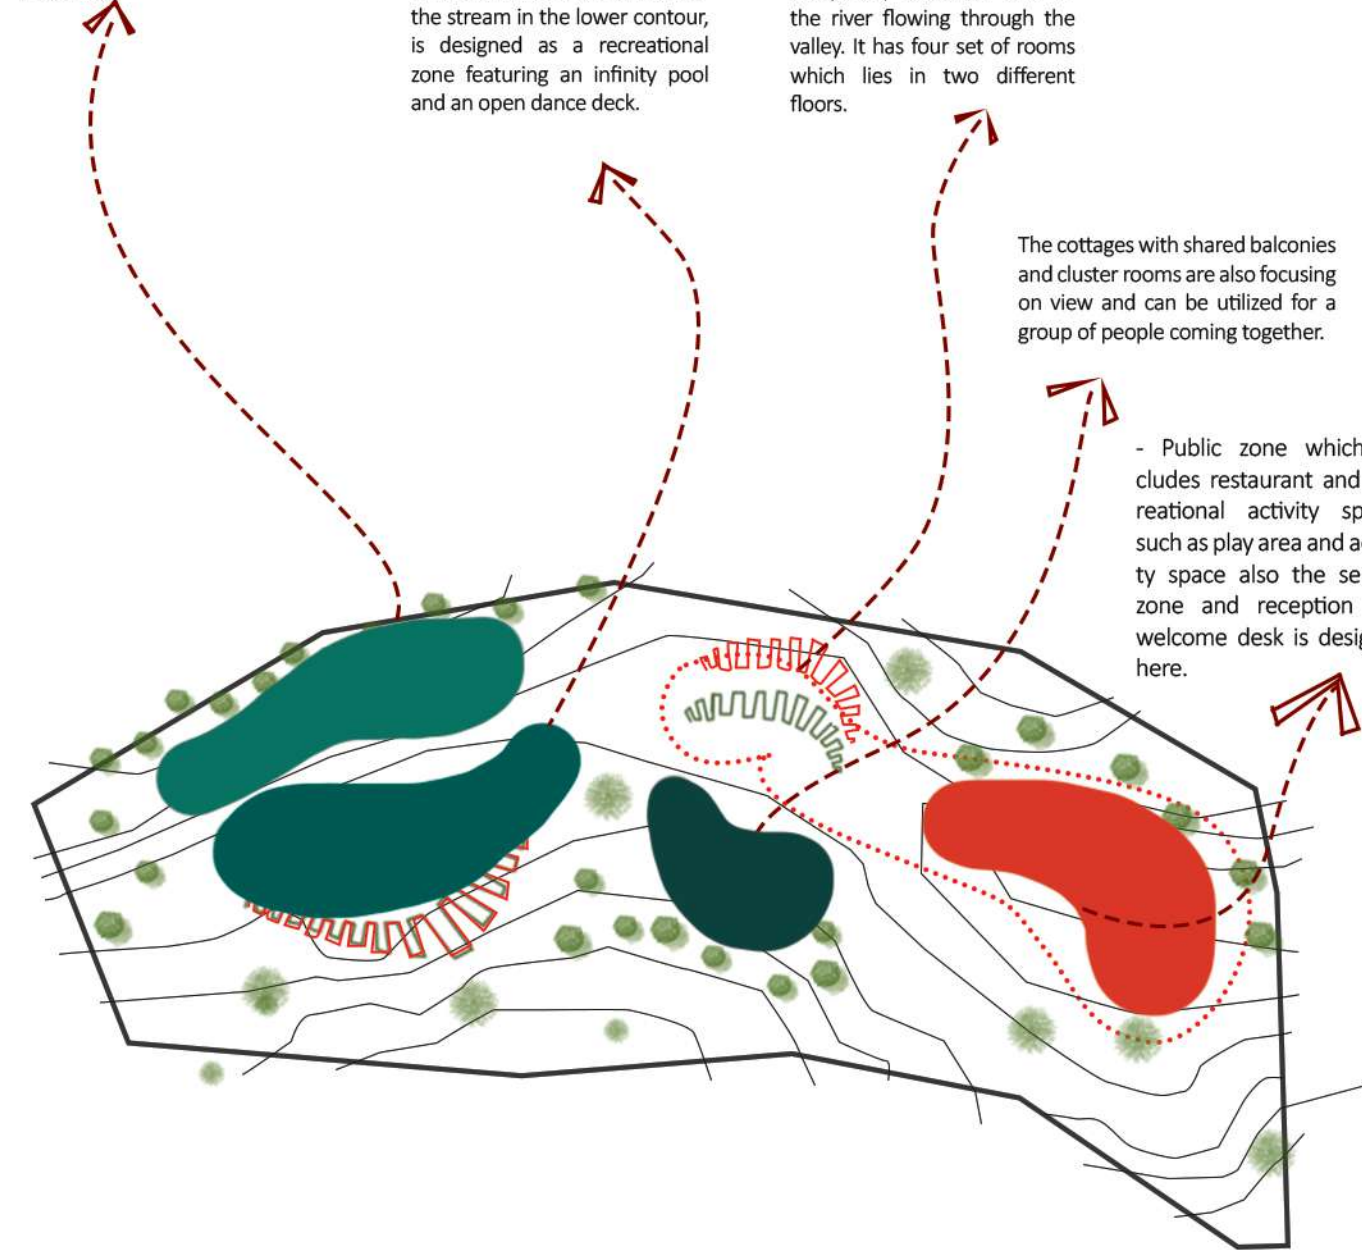

1. ENTRANCE / SECURITY
2. WALKWAY
3. FOYER
4. RECEPTION BLOCK
 - LEVEL-1 : GAMES ROOM/ TOILET
 - LEVEL-2(ENTRY) : RECEPTION/LOUNGE/BOUTIQUE
 - LEVEL-3 : ADMIN BLOCK

5. BRIDGE
6. RESTAURANT BLOCK
 - LEVEL-1 : RESTAURANT/ KITCHEN
 - LEVEL-2(ENTRY) : BAR
 - LEVEL-3 : BANQUET HALL
7. DELUXE ROOM : (15 Nos.) @ 3 LEVELS

8. POOL/ DECK
9. HEALTH CLUB
10. PREMIUM ROOM
 - GF-2/ FF-2 : (16NOS.)
11. VILLA : (4 NOS.)

06 Interior Design.

CLIENT | ANISH RAJAN

SITE | BENGALURU

Introduction.

The living space is designed with a contemporary aesthetic that emphasizes clean architectural elements, minimal detailing, and a refined material palette. Neutral tones combined with carefully selected textures create a warm and inviting atmosphere while maintaining a sense of elegance and sophistication. The design focuses on openness, natural light, and balanced spatial planning to achieve a comfortable yet visually refined living environment.





07 Interior Fit Out

CLIENT | FOLK MARITIME GROUP | SAUDI ARABIA

Introduction.

Folk Maritime was a challenging project despite its compact area of approximately 430 sq.ft. Beyond managing the client-side project requirements, the most valuable part of the experience was coordinating and learning through direct interaction with the consultant group JANA. Every element within the project was carefully designed and precisely executed with strong attention to detail and design integration.

MoodBoard




08 Interior Fit Out

CLIENT | ARCELORMITTAL GROUP | SAUDI ARABIA

Introduction.

ArcelorMittal was another challenging project focused on transforming the client's requirements into a breathable and efficient workstation environment. Integrating all functional requirements within the space planning was the most demanding aspect of the project. Overall, it became one of the most satisfying projects after execution and completion.

MoodBoard

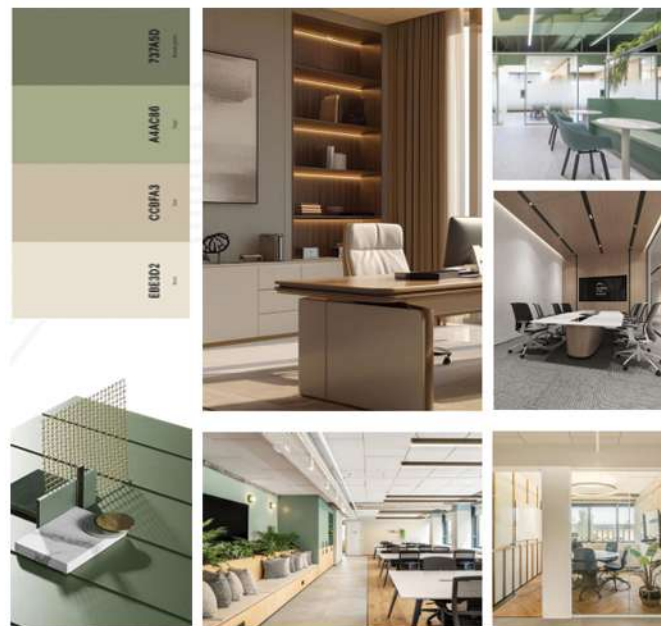

Visual representations were generated in collaboration with 3D visualizer I



09 Interior Fit Out

CLIENT | AL WAHA GROUP | SAUDI ARABIA


Introduction.

Alwaha was a compact two-level office project designed with subtle yet impactful design elements. The space was carefully planned and executed to reflect the client's vision while maintaining a clean and functional work environment.

MoodBoard

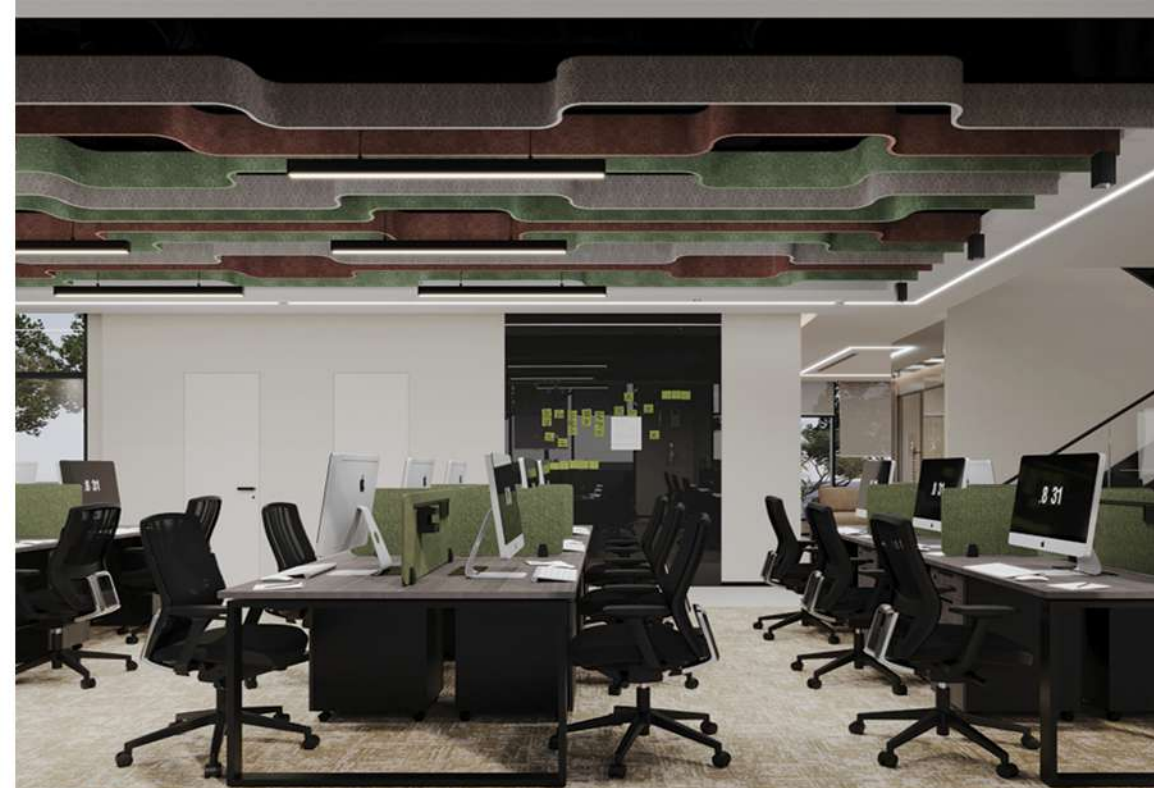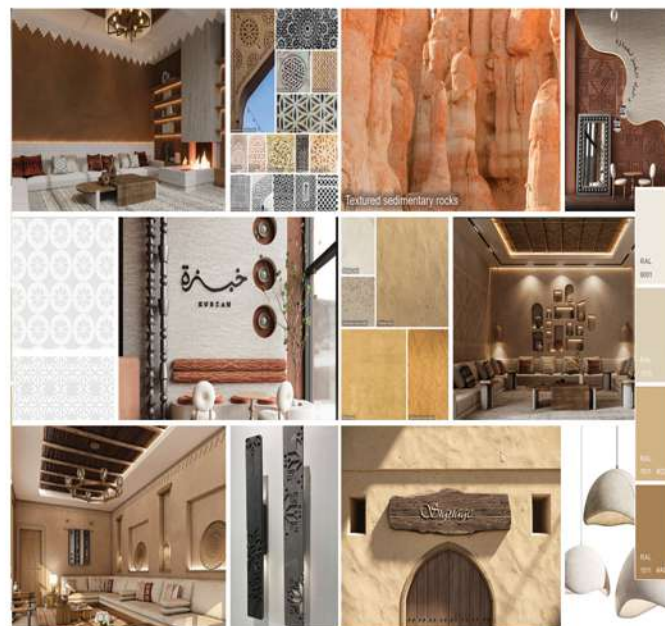

10 Miscellaneous

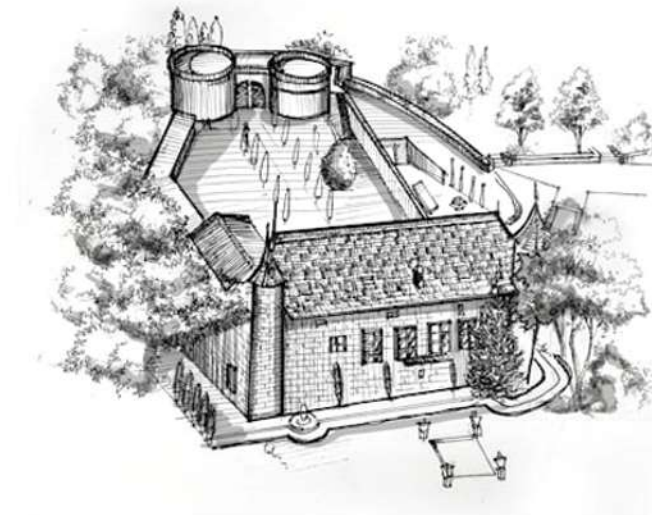

Sketches & Works

MALAVIKA NAIR
malavika.arch@gmail.com
7676878778